


$\frac{0,91}{1,89}$	Türdemakung Breite/Höhe
$\frac{1,20}{2,25}$	Fensterdemakung Breite/Höhe + Brüstungshöhe
R	Raumhöhe

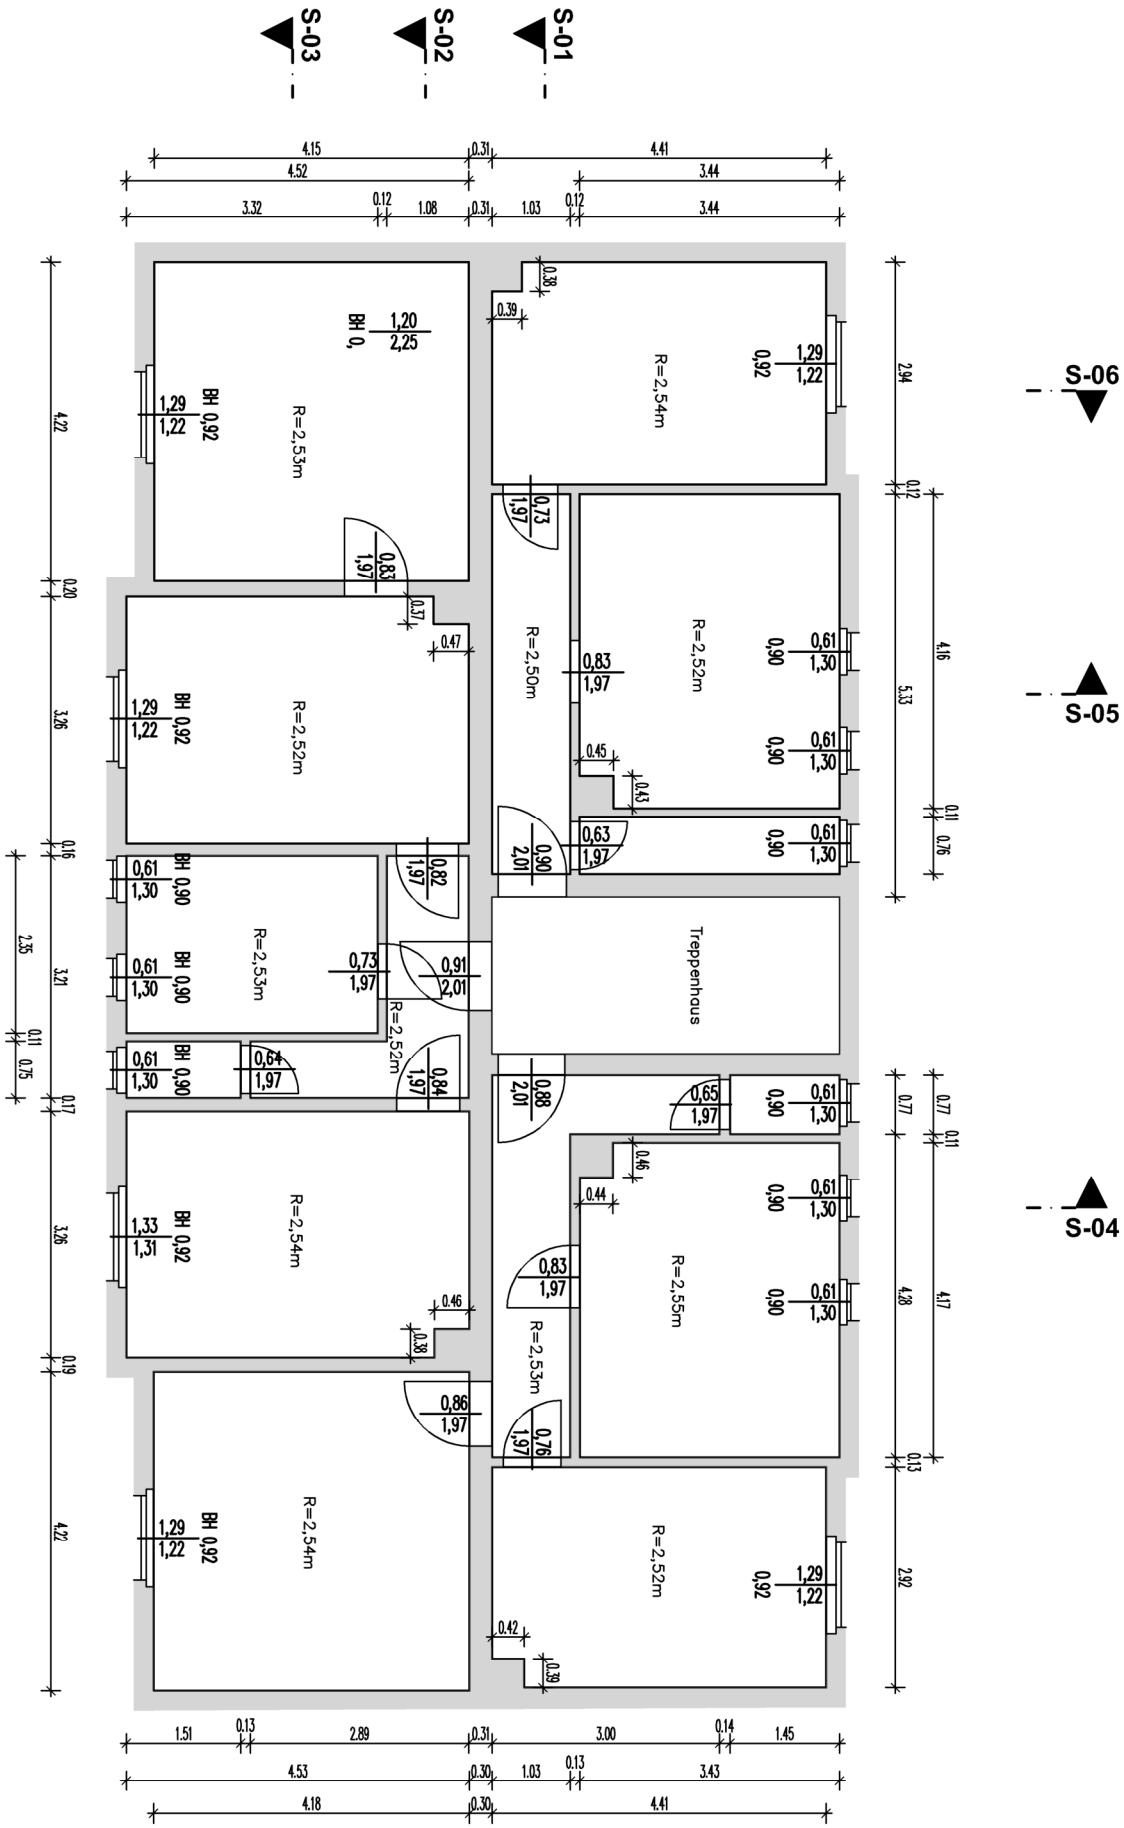

**VERMESSUNGS- UND
INGENIEURGESELLSCHAFT mbH**
Pfeilstraße 9 · 04249 Leipzig
Tel.: 0341/49070-0 · e-mail: info@vermessungen.de

Hasenheide 4
1. Obergeschoss

Auftraggeber BrandschutzConsult Ingenieurgesellschaft mbH Leipzig Torgauer Platz 3 04315 Leipzig	Masstab 1 : 100	Gem. 27.11.2025
Auftrag Nr. 25103-01	März	
Bearbeiter Dechandt	Leipzig, den 01.12.2025	